


总体设计范围总览平面

范围、用地、绿地与三处重点区域均由本包 geometry/ 图层投影生成；边界为组织方临时粗略范围，不作红线依据。

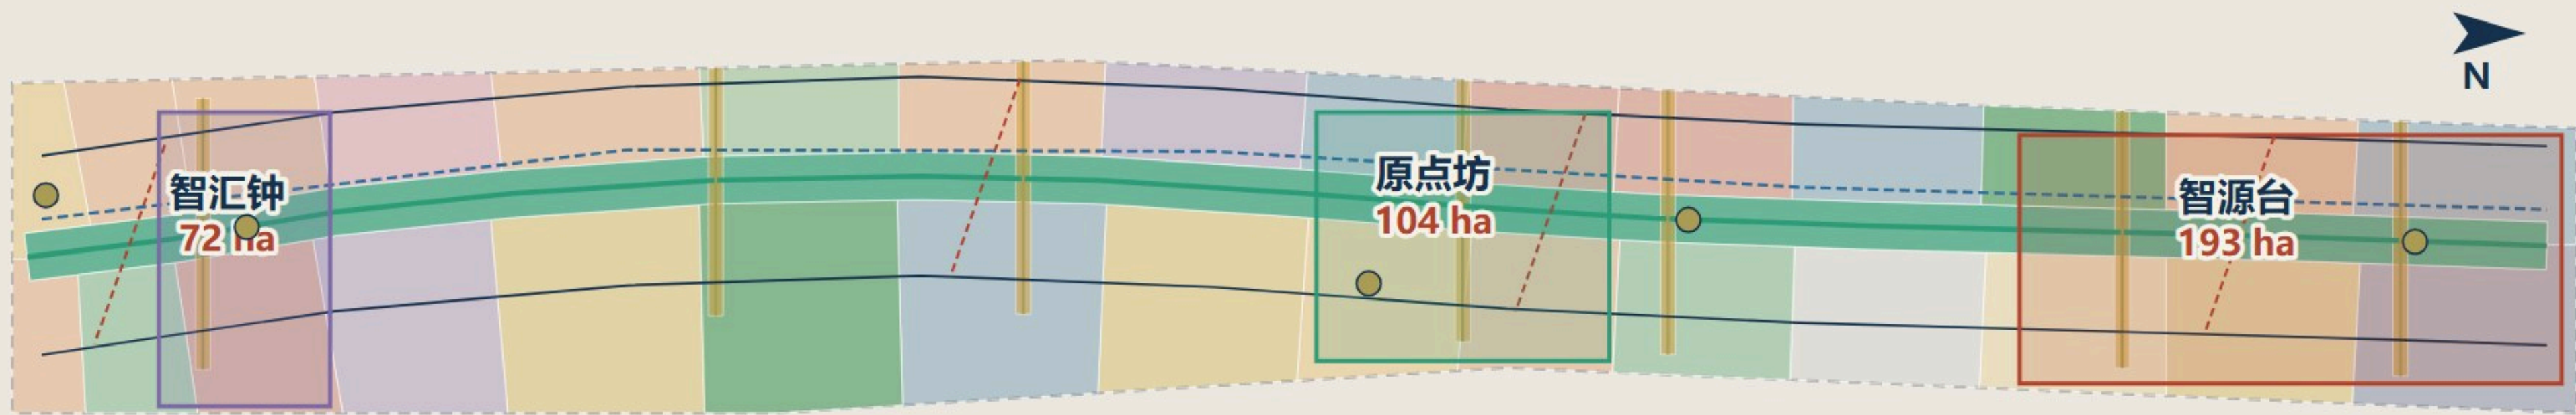

0 500 1000 1500 2000 m

- 总体设计范围（临时粗略）
- 重点区域
- 遗址公园主脉绿廊
- 主绿道（慢行主轴）
- 通勤自行车道
- 东西缝合步行链
- 次干路
- 智站接驳线
- 朝圣地标


总体设计范围面积: 11.35 km2 | 按 metrics.json site_area_sqm 复算一致

.01

? ??????1909????????????????????2026???AI?????????????
? 4?????????1909?????????1949?????????1980?????????2026??????
? ??????????????????????+ ??????????????????????

用地结构平面（街区级）

31 个地块按用地代码着色，图例与面积统计均由 land_use.geojson 复算。

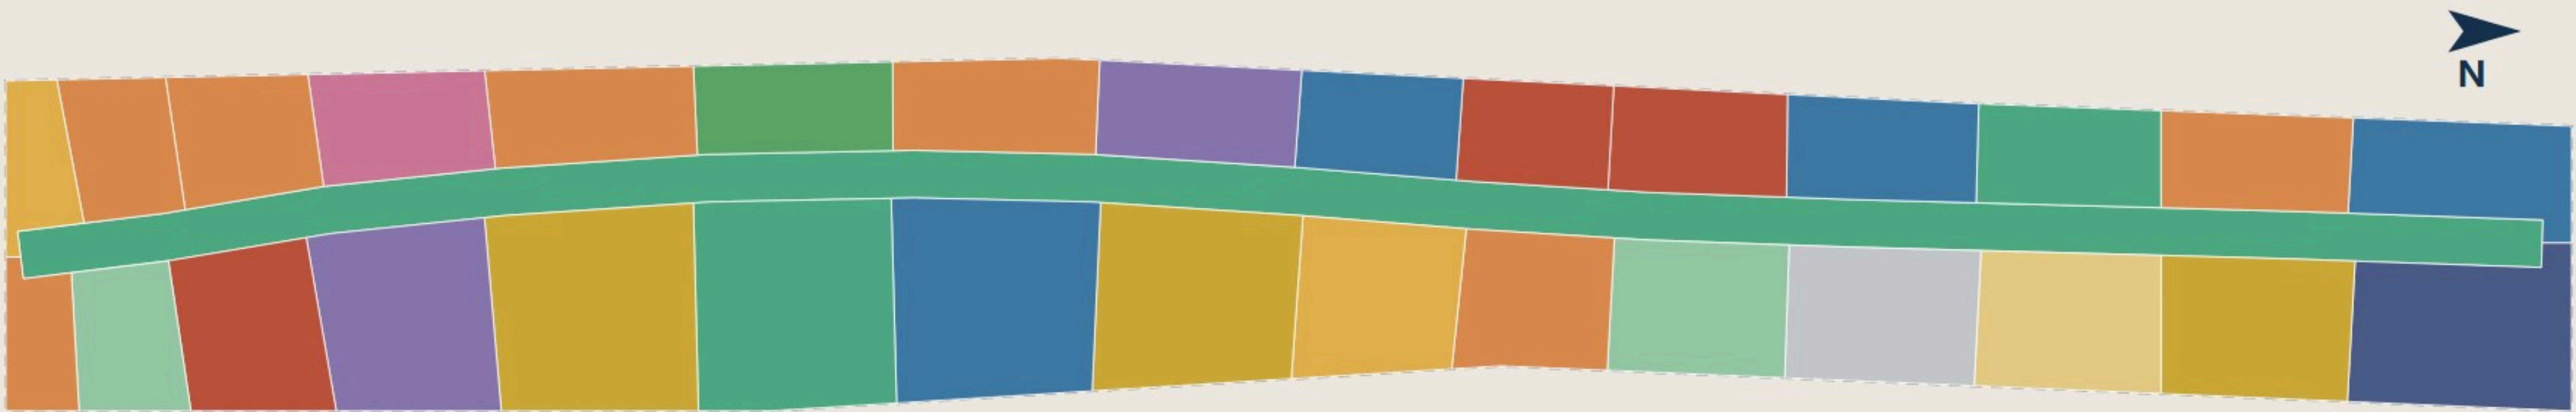

0 500 1000 1500 2000 m

- 公园绿地
- 商业服务业用地
- 城镇住宅用地
- 科研用地
- 文化用地
- 教育用地
- 防护绿地
- 广场用地
- 公共管理与公共服务用地
- 留白用地
- 城镇社区服务设施用地
- 医疗卫生用地
- 体育用地

用地面积统计（由 land_use.geojson 复算）

代码	用地类别	面积 (ha)	占比
1401	公园绿地	257.1	22.5%
05	商业服务业用地	169.7	14.9%
0701	城镇住宅用地	147.0	12.9%
0802	科研用地	138.7	12.2%
0803	文化用地	81.8	7.2%
0804	教育用地	73.1	6.4%
1402	防护绿地	55.1	4.8%

代码	用地类别	面积 (ha)	占比
1403	广场用地	49.4	4.3%
08	公共管理与公共服务用地	45.7	4.0%
16	留白用地	36.5	3.2%
0702	城镇社区服务设施用地	35.9	3.1%
0806	医疗卫生用地	26.4	2.3%
0805	体育用地	25.0	2.2%

合计 1141.3 ha (31 个地块)


.02

? ??????4???TOD?14????????????11.41 km²?????????????????
? ??
? ?????????? geometry/ ??? EPSG:4548 ??????????????????????


三处重点区域放大平面

街区轮廓 = 地块边界；公共空间、主要街道与答卷亭点位均落位于图上（点位示意）。


智源台 Origin Terrace

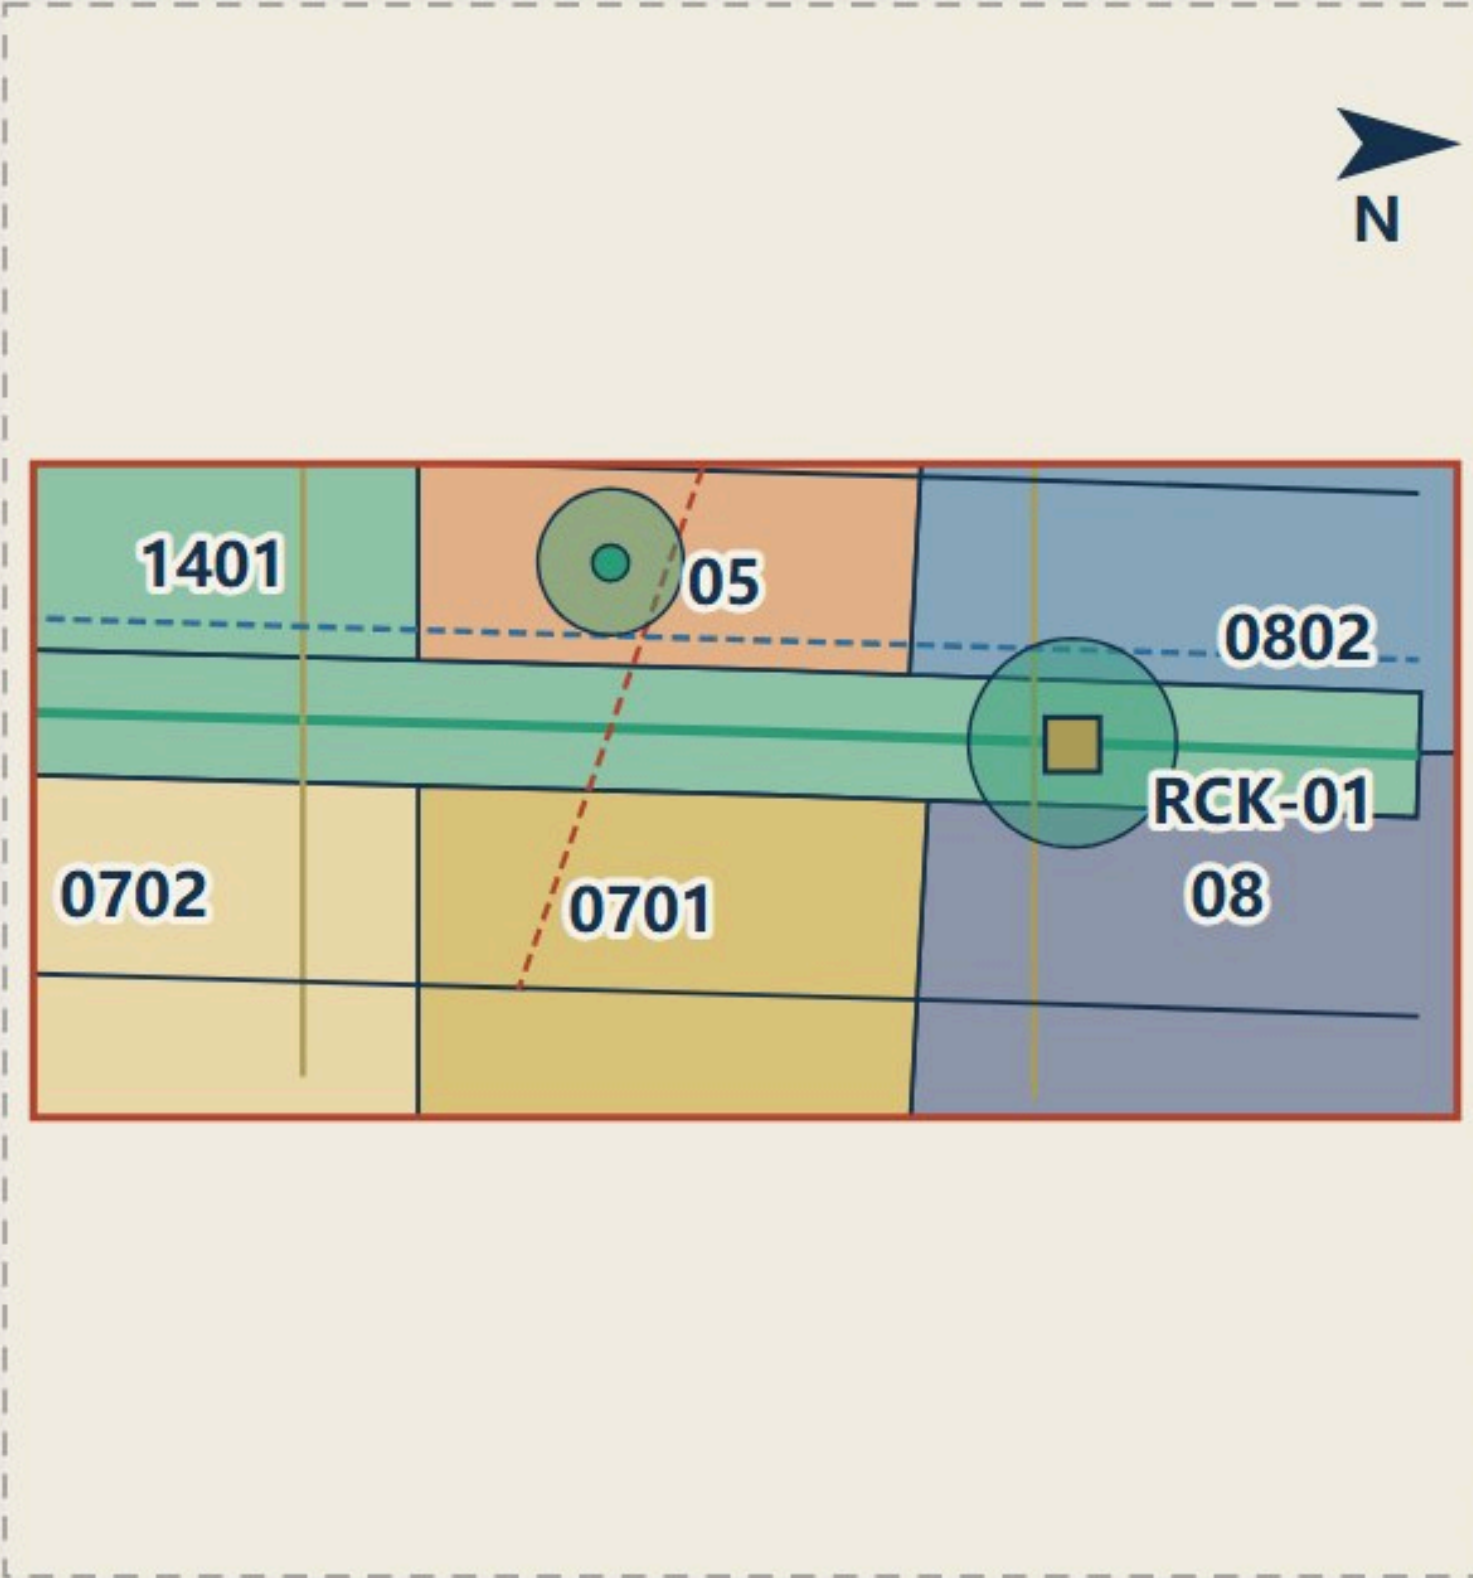


片区面积 192.92 ha

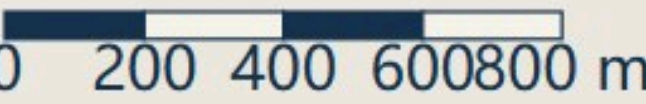


原点坊 Origin Works

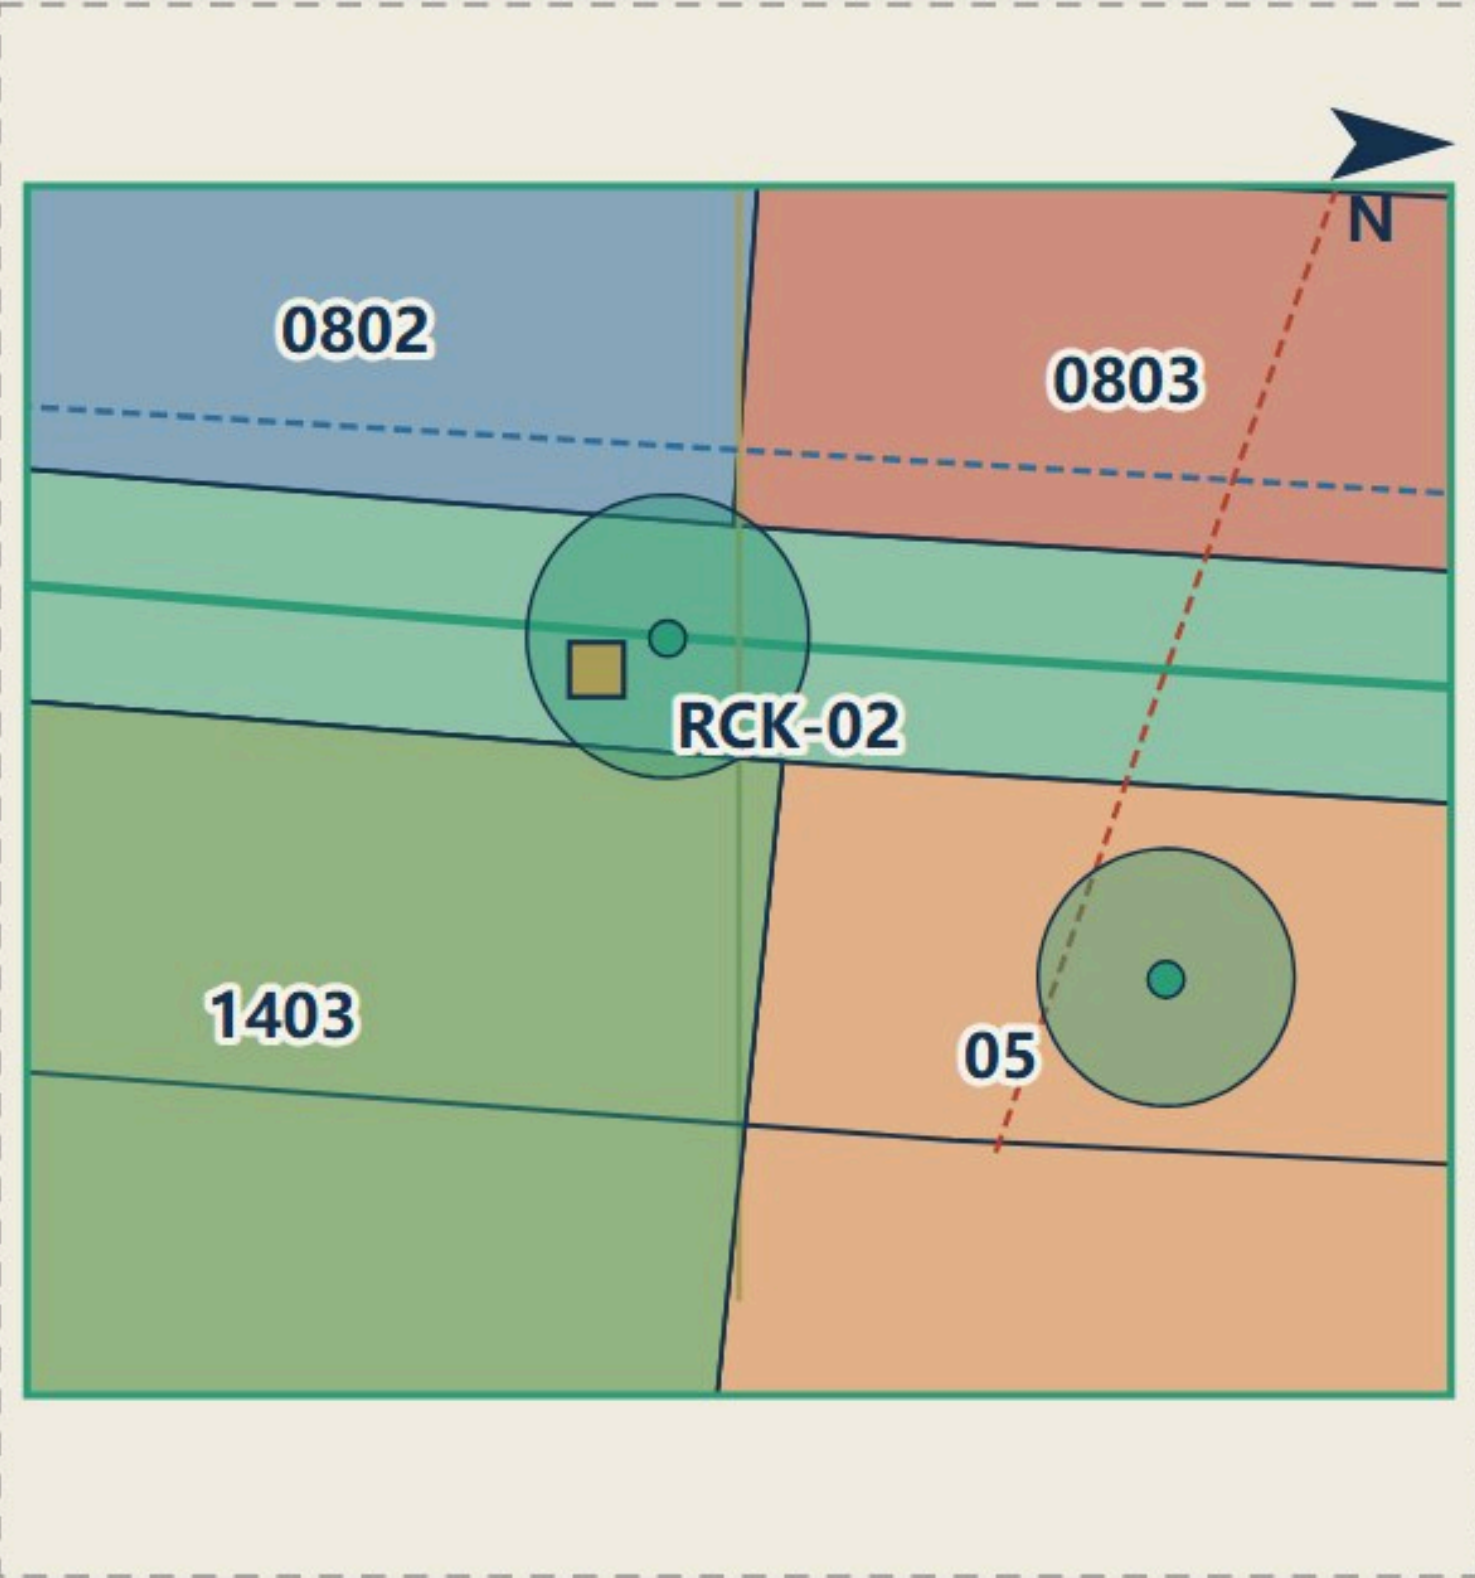

片区面积 104.32 ha

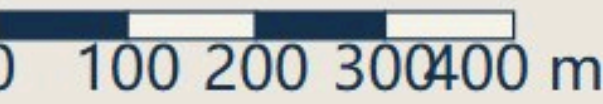

智汇钟 Bell Hub

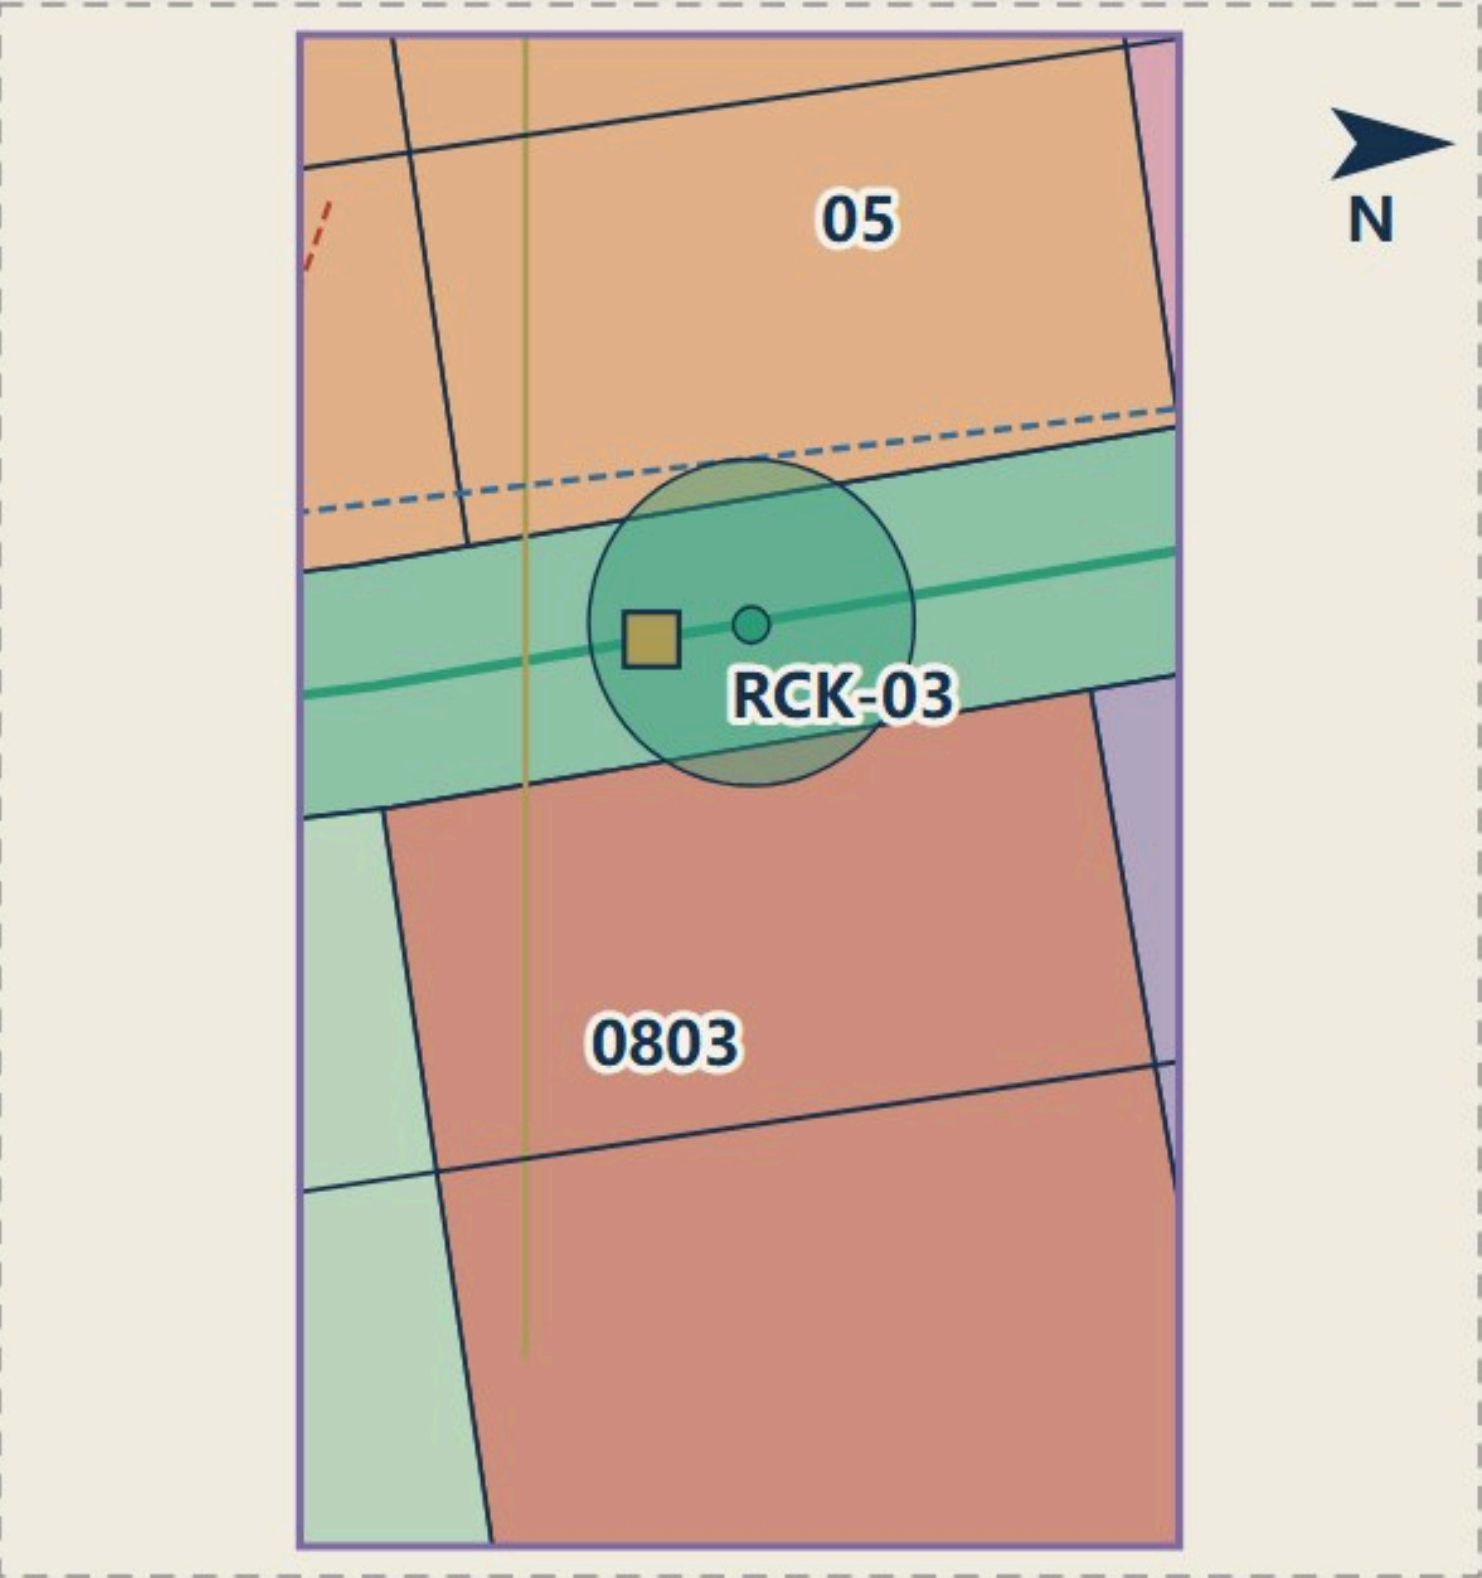

片区面积 72.05 ha



街区轮廓（地块） 公共空间节点 主要街道 答卷亭点位

街区轮廓标注为用地代码；答卷亭点位取自 proposal.md 部署计划表。

... ..193 ha·

????ZZ-A??????ZZ-B??????ZZ-C??????ZZ-D??????ZZ-E??????
??????? 1.6?3.5???? 24?60 m????? ?35%?
??????????????? + ???TOD + RCK-01 ??????
??????????? 30.0 m/ha????? 5,791 m???? ?85%?

... ..Al.....104 ha·



????YD-A??????YD-B??????YD-C??????YD-D??????YD-E??????
??????? 1.2?2.8???? 18?45 m????? ?35%?
???????????????+ ????????????+ RCK-02 ????
??????????? 29.6 m/ha????? 3,092 m?????????

... ..Al....72 ha·

????DZ-A??????DZ-B??????DZ-C??????DZ-D????DZ-E??????
??????? 1.8?3.6???? 24?60 m????? ?35%?
???????????????????+ ?????????? + RCK-03 ????
??????????? 31.7 m/ha????? 2,283 m?????????


慢行、蓝绿与水系叠合平面

骑行网络、步行优先、绿廊与滨水四层叠加在同一底图上，各层图例分列于下。

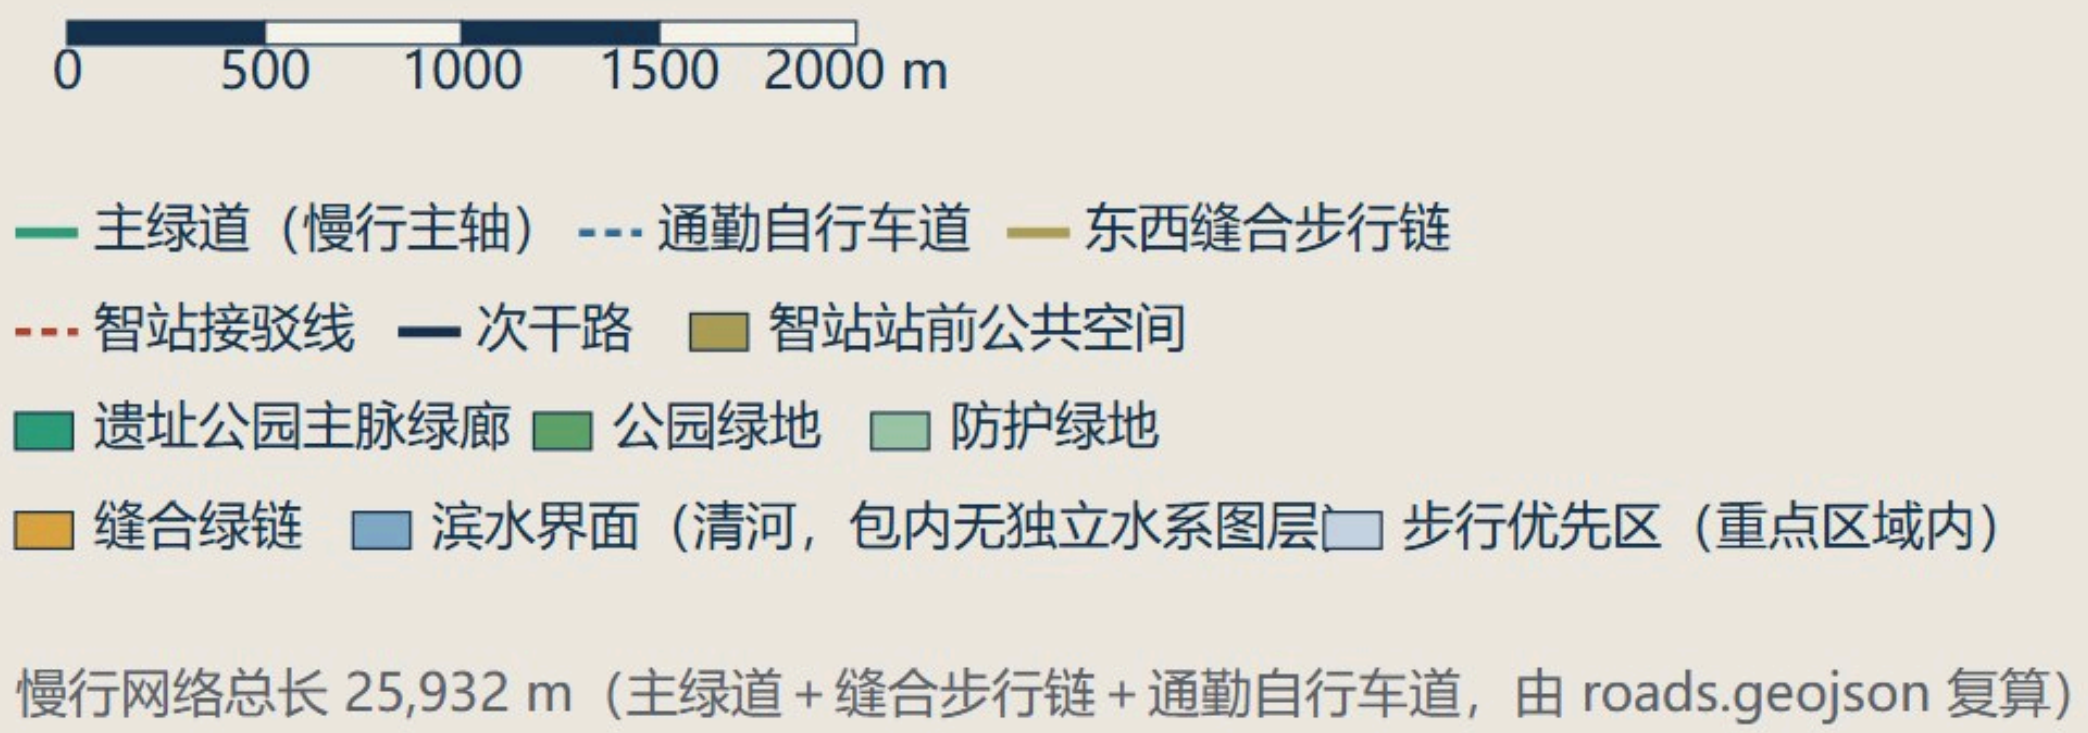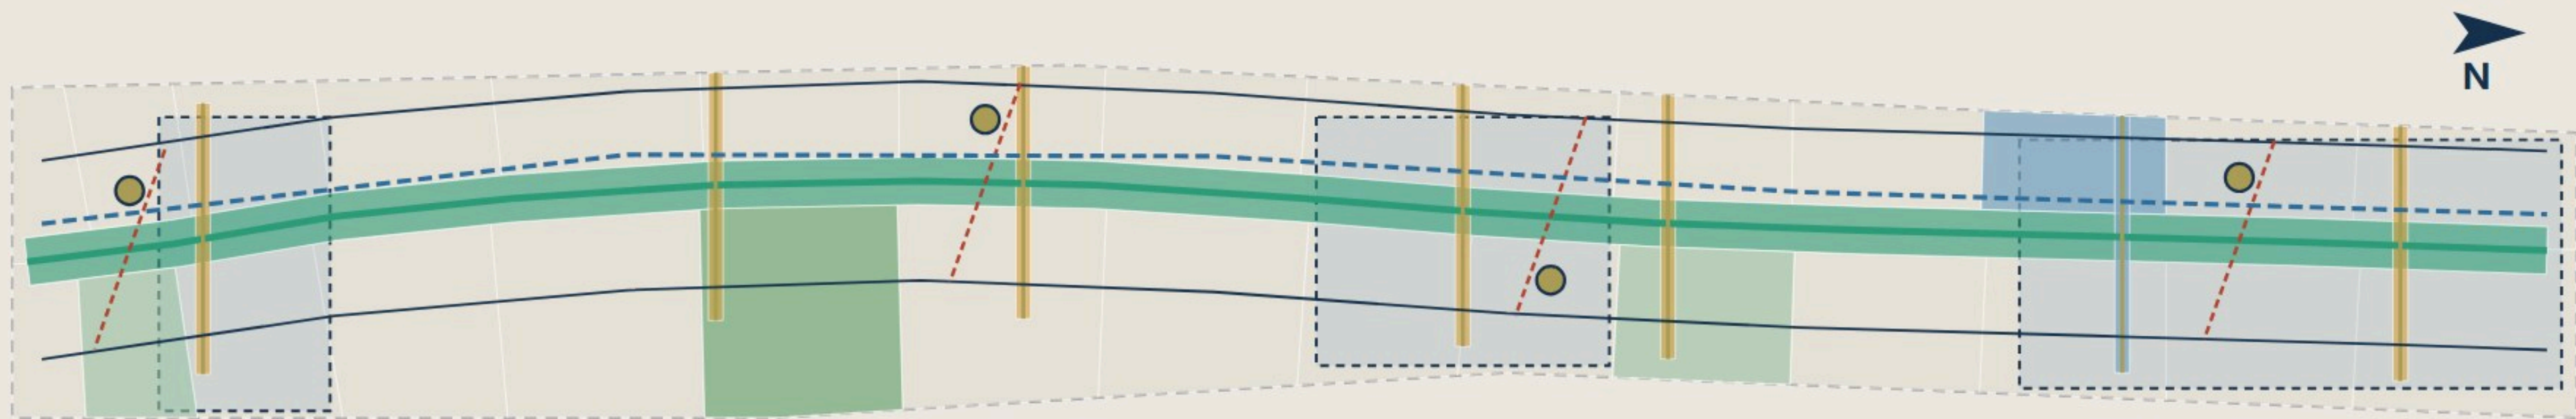

指标图证：三片区等面积方形图解与复算值

每个方形的边长按片区实际面积开方绘制，面积、慢行里程与比率均由本包 geometry/ 图层复算

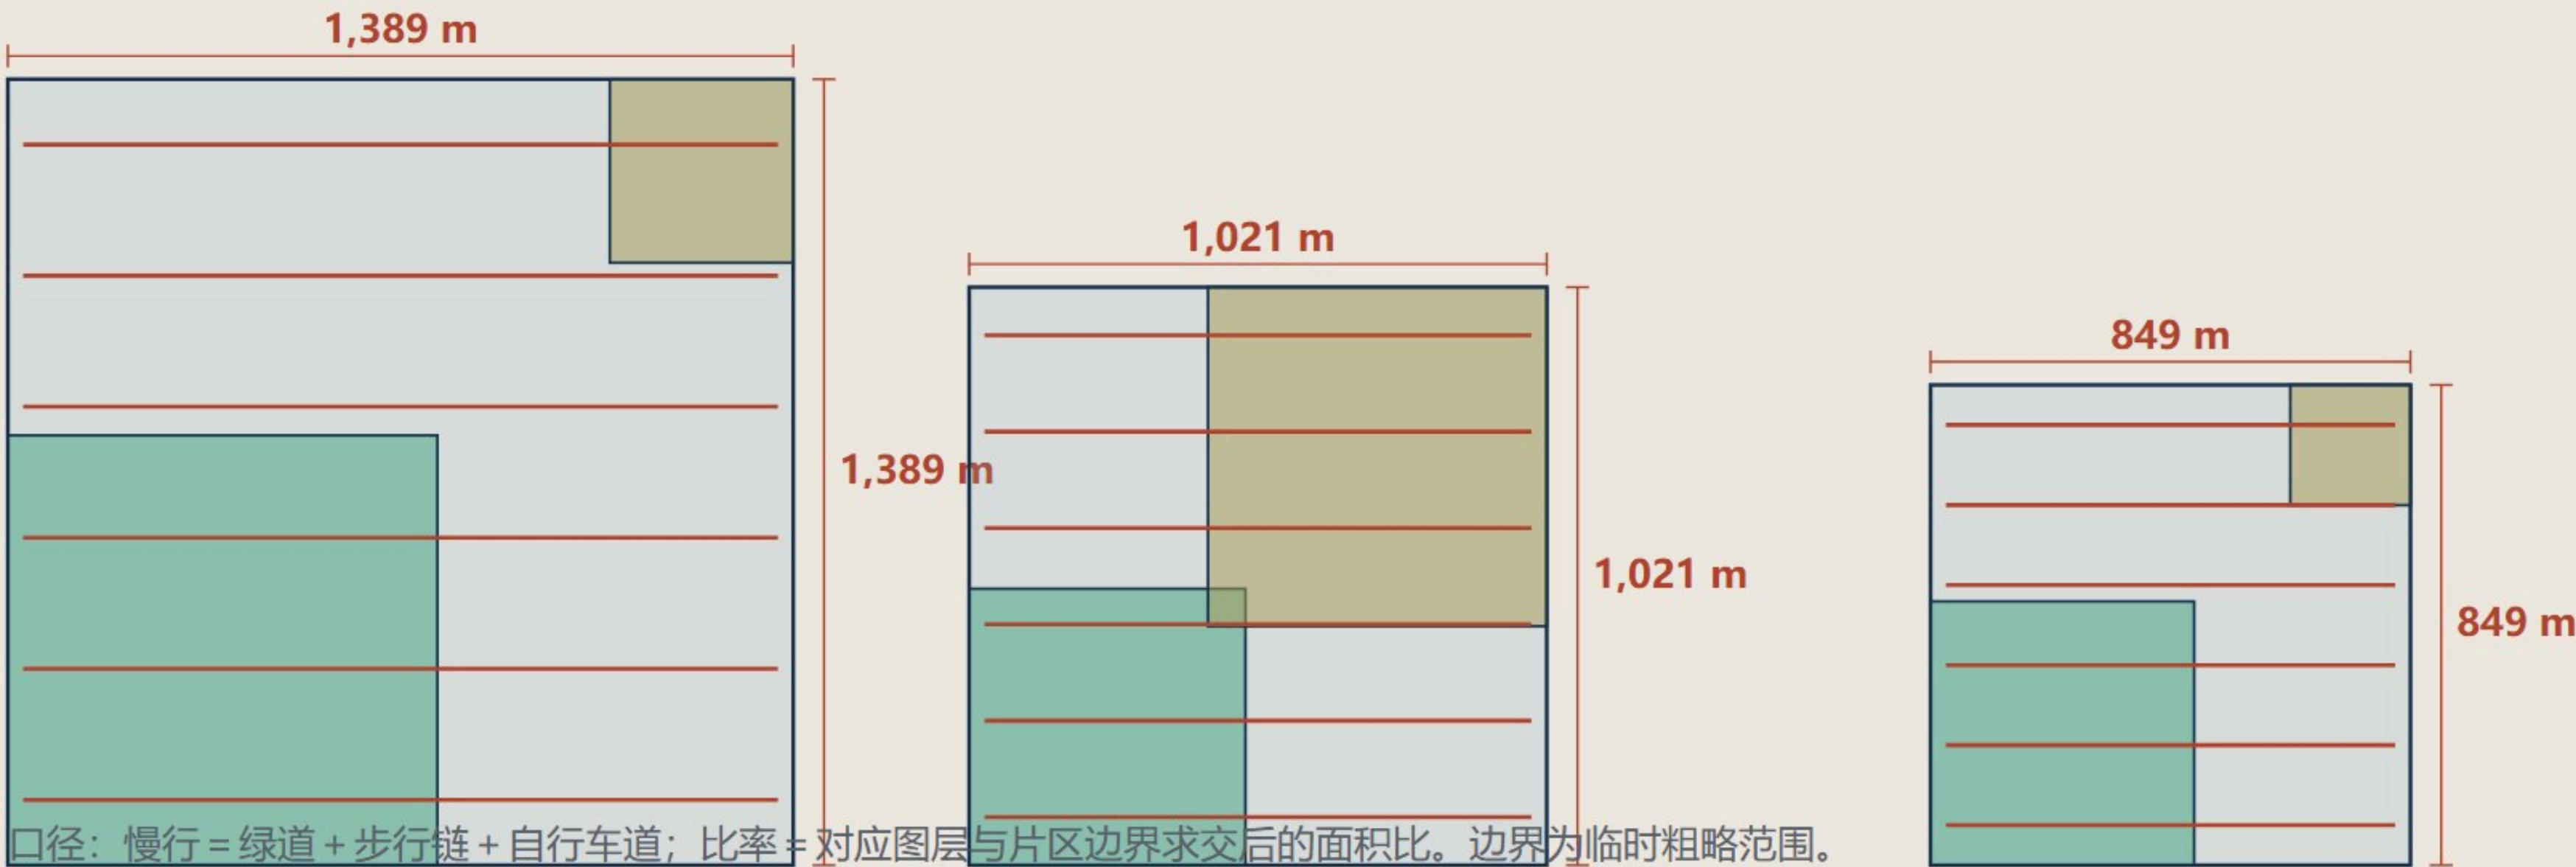

口径：慢行 = 绿道 + 步行链 + 自行车道；比率 = 对应图层与片区边界求交后的面积比。边界为临时粗略范围。

智源台（众智园）

面积	192.92 ha
等效边长	1,389 m
慢行里程	5,791 m
慢行密度	30.0 m/ha
绿地率	29.9%
公共空间占比	5.5%
建筑覆盖率	9.2%
通勤自行车道	2,000 m
站点接驳线	797 m

■ 面积 ■ 绿地率 ■ 公共空间占比 — 慢行里程

原点坊（AI原点社区）

面积	104.32 ha
等效边长	1,021 m
慢行里程	3,092 m
慢行密度	29.6 m/ha
绿地率	22.9%
公共空间占比	34.4%
建筑覆盖率	8.3%
通勤自行车道	1,112 m
站点接驳线	797 m

智汇钟（大钟寺）

面积	72.05 ha
等效边长	849 m
慢行里程	2,283 m
慢行密度	31.7 m/ha
绿地率	30.2%
公共空间占比	6.3%
建筑覆盖率	10.5%
通勤自行车道	653 m
站点接驳线	66 m

·04

? ?????9.0 km ?????????????? + ??????????????

? ???

? ?????4??? 500m ??????????50m????????????????? ?40%?

·05

? 33?????30????????????????????? ? ?????3????????????? unknown?

? ?????????? 3.96 m²?1800×2200×2800 mm????????32?????+???????????????

? ?????????????????????????????????????30????? 100% ???